

DOCUMENTO FICTÍCIO — BASE SINTÉTICA DO ARQUITETO AUDITOR — NÃO CORRESPONDE A IMÓVEL REAL

QUADRO DE ESQUADRIAS

P1	0,90 x 2,10	PORTA DE GIRO — ENTRADA
P2	0,80 x 2,10	PORTA DE GIRO — MADEIRA
P3	0,70 x 2,10	PORTA DE GIRO — ÁREAS MOLHADAS
PG	2,80 x 2,20	PORTÃO BASCULANTE
J1	1,50 x 1,20	JANELA DE CORRER — PEITORIL 1,00
J2	0,60 x 0,60	BASCULANTE — PEITORIL 1,60

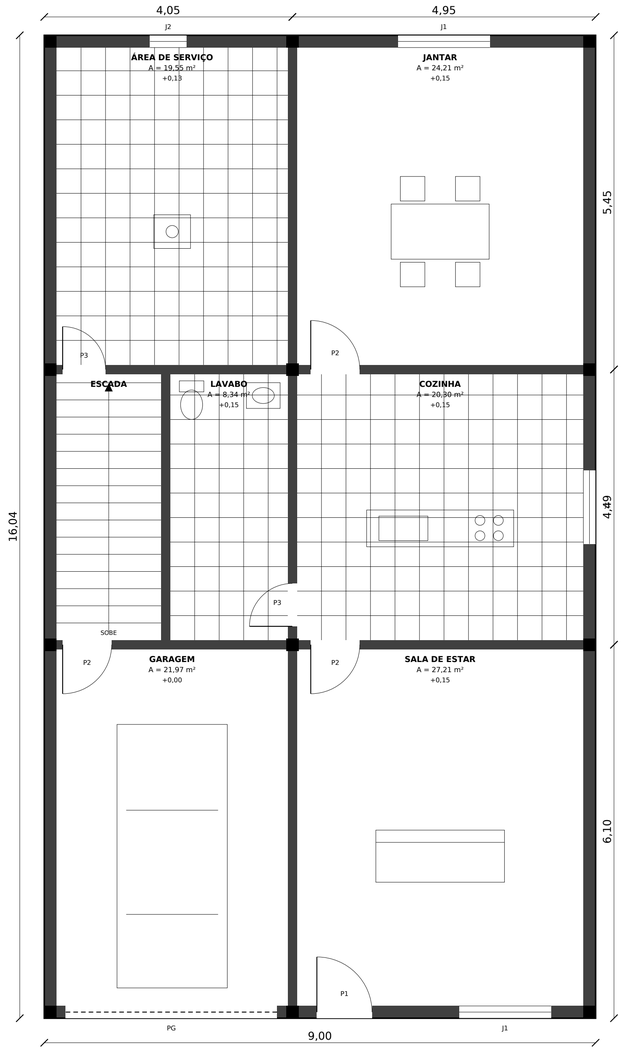

PLANTA BAIXA — TÉRREO — ESCALA 1:50
ÁREA: 144,36 m²

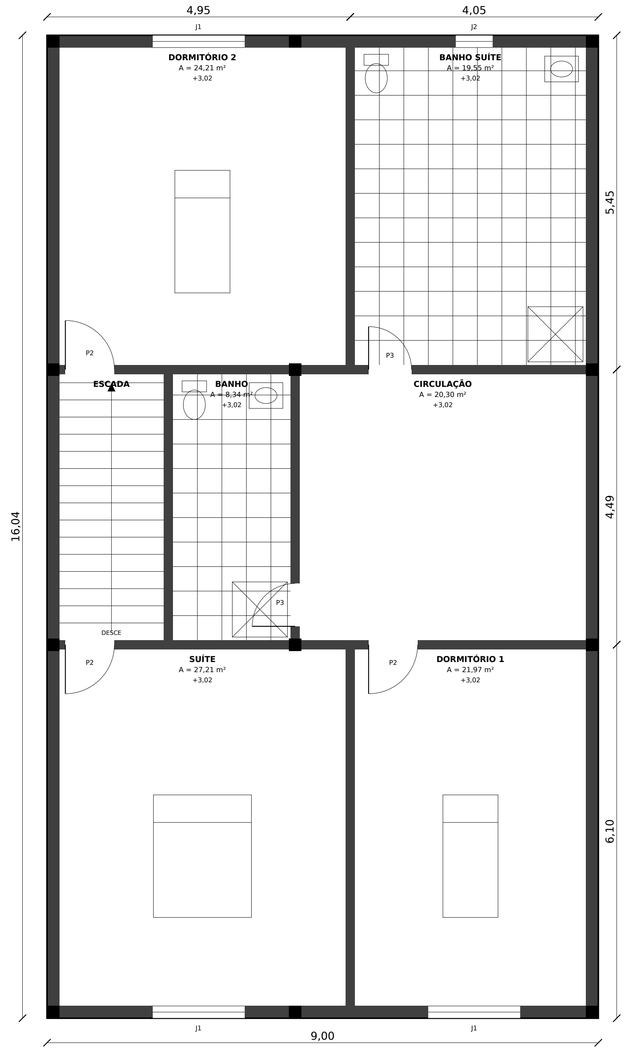

PLANTA BAIXA — PAVIMENTO SUPERIOR — ESCALA 1:50
ÁREA: 115,49 m²

R00	15/09/2026	EMISSÃO INICIAL

ESCRITÓRIO:	Oficina Almeida Arquitetura
OBRA:	RESIDÊNCIA SIQUEIRA
LOCAL:	Rua das Palmeiras, 836
CONDOMÍNIO:	Residencial Costa
LOTE / QUADRA:	2 / C
MUNICÍPIO:	Vila Almeida
Nº MAT.:	96.932 — 1º Ofício de Registro de Imóveis de Vila Almeida
INTERESSADO:	
RESP. TÉCNICO:	Rafael Gonçalves Farias
REG. PROF.:	CAU A129339-6
RRT Nº:	15547257
CONTEÚDO:	PLANTAS BAIXAS
FOLHA:	02/03
REV.:	R00
ESCALA:	INDICADA
DATA:	15/09/2026

AUTOR DO PROJETO

PROPRIETÁRIO