

DOCUMENTO FICTÍCIO — BASE SINTÉTICA DO ARQUITETO AUDITOR — NÃO CORRESPONDE A IMÓVEL REAL

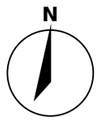

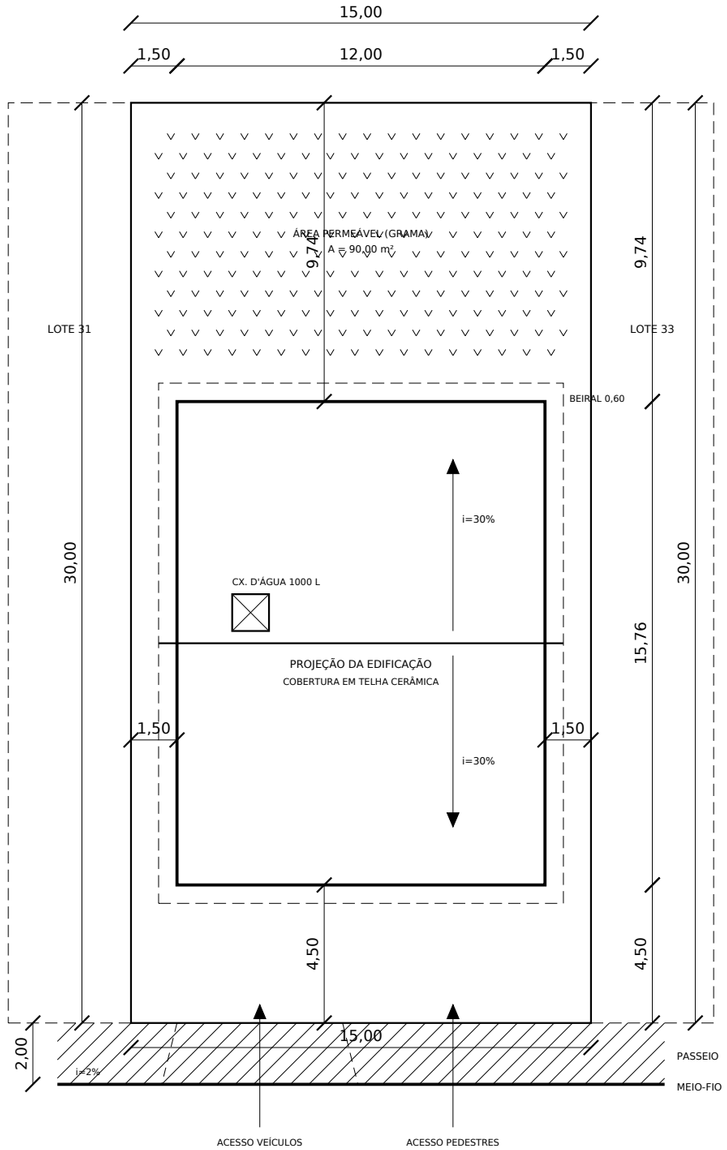

AVENIDA DOS IPÊS


PLANTA DE SITUAÇÃO — ESCALA 1:200

QUADRO DE ÁREAS

450,00 m²	— ÁREA DO LOTE
189,12 m²	— ÁREA COBERTA TÉRREO
151,30 m²	— ÁREA 1º PAVIMENTO
340,42 m²	— ÁREA TOTAL CONSTRUÍDA
189,12 m²	— PROJEÇÃO
90,00 m²	— ÁREA PERMEÁVEL
42,03 %	— ÍNDICE DE OCUPAÇÃO
0,76	— ÍNDICE DE APROVEITAMENTO
20,00 %	— ÍNDICE DE PERMEABILIDADE

PLANTA DE LOCALIZAÇÃO

SEM ESCALA

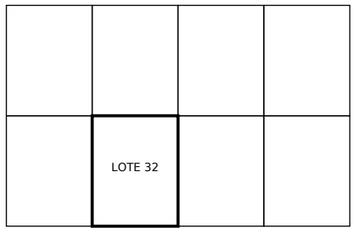

QUADRA F — Residencial Mendes

ESCRITÓRIO

Grupo Monteiro Arquitetura

PROJETO

RESIDÊNCIA ALMEIDA

ENDEREÇO

Avenida dos Ipês, 202

CONDOMÍNIO

Residencial Mendes

LOTE / QUADRA

32 / F

MUNICÍPIO

Campo Santos

MATRÍCULA

73.796 — 2º Ofício de Registro de Imóveis de Campo Santos

PROPRIETÁRIO

Valentim Azevedo Correia

AUTOR DO PROJETO

Sara Melo Araújo

REGISTRO

CAU A286237-7

RRT

10951015

CONTEÚDO

SITUAÇÃO E LOCALIZAÇÃO

PRANCHA

01/03

REVISÃO

R00

ESCALA

INDICADA

DATA

15/09/2026


AUTOR DO PROJETO

PROPRIETÁRIO

DOCUMENTO FICTÍCIO — BASE SINTÉTICA DO ARQUITETO AUDITOR — NÃO CORRESPONDE A IMÓVEL REAL


QUADRO DE ESQUADRIAS

P1	0,90 x 2,10	PORTA DE GIRO — ENTRADA
P2	0,80 x 2,10	PORTA DE GIRO — MADEIRA
P3	0,70 x 2,10	PORTA DE GIRO — ÁREAS MOLHADAS
PG	2,80 x 2,20	PORTÃO BASCULANTE
J1	1,50 x 1,20	JANELA DE CORRER — PEITORIL 1,00
J2	0,60 x 0,60	BASCULANTE — PEITORIL 1,60

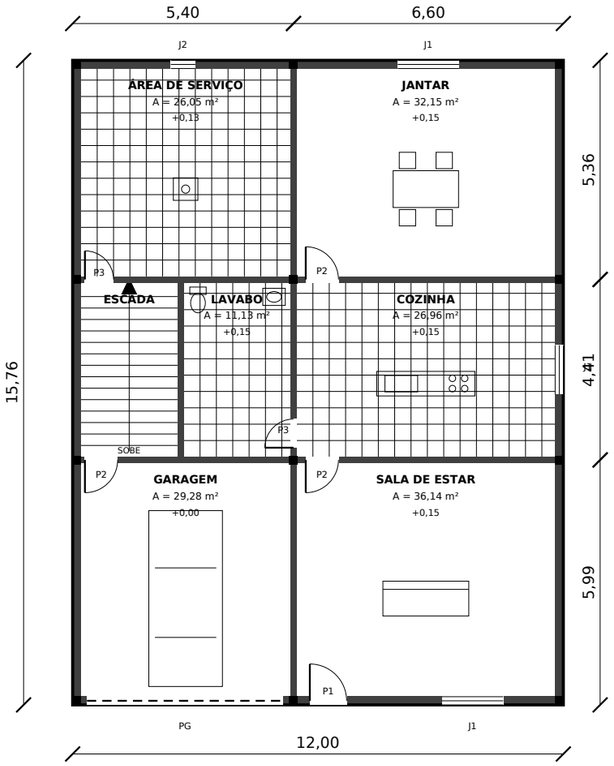

PLANTA BAIXA — TÉRREO — ESCALA 1:150

ÁREA: 189,12 m²

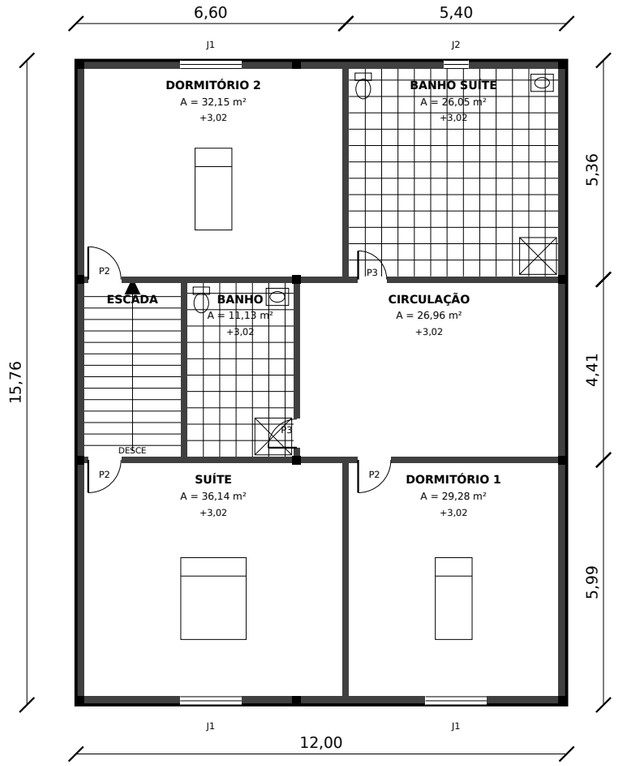

PLANTA BAIXA — PAVIMENTO SUPERIOR — ESCALA 1:150

ÁREA: 151,30 m²

ESCRITÓRIO

Grupo Monteiro Arquitetura

PROJETO

RESIDÊNCIA ALMEIDA

ENDEREÇO

Avenida dos Ipês, 202

CONDOMÍNIO

Residencial Mendes

LOTE / QUADRA

32 / F

MUNICÍPIO

Campo Santos

MATRÍCULA

73.796 — 2º Ofício de Registro de Imóveis de Campo Santos

PROPRIETÁRIO

Valentim Azevedo Correia

AUTOR DO PROJETO

Sara Melo Araújo

REGISTRO

CAU A286237-7

RRT

10951015

CONTEÚDO

PLANTAS BAIXAS

PRANCHA

02/03

REVISÃO

R00

ESCALA

INDICADA


DATA

15/09/2026


AUTOR DO PROJETO

PROPRIETÁRIO

DOCUMENTO FICTÍCIO — BASE SINTÉTICA DO ARQUITETO AUDITOR — NÃO CORRESPONDE A IMÓVEL REAL

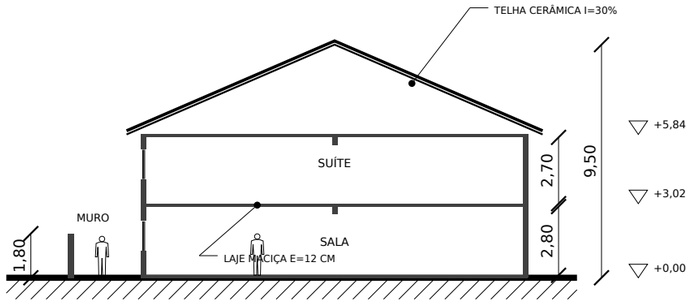

CORTE AA — ESCALA 1:250

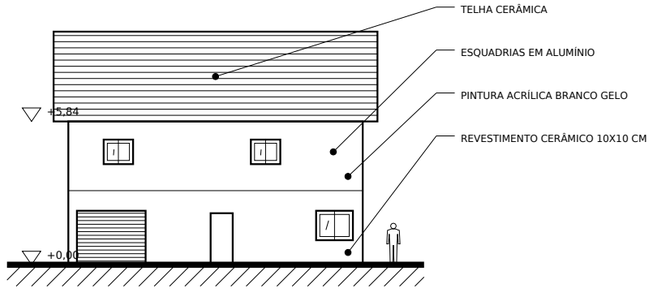

FACHADA FRONTAL — ESCALA 1:250

ESCRITÓRIO

Grupo Monteiro Arquitetura

PROJETO

RESIDÊNCIA ALMEIDA

ENDEREÇO

Avenida dos Ipês, 202

CONDOMÍNIO

Residencial Mendes

LOTE / QUADRA

32 / F

MUNICÍPIO

Campo Santos

MATRÍCULA

73.796 — 2º Ofício de Registro de Imóveis de Campo Santos

PROPRIETÁRIO

Valentim Azevedo Correia

AUTOR DO PROJETO

Sara Melo Araújo

REGISTRO

CAU A286237-7

RRT

10951015

CONTEÚDO

CORTE E FACHADA

PRANCHA

03/03

REVISÃO

R00

ESCALA

INDICADA

DATA

15/09/2026

AUTOR DO PROJETO

PROPRIETÁRIO