
DOCUMENTO FICTÍCIO — BASE SINTÉTICA DO ARQUITETO AUDITOR — NÃO CORRESPONDE A IMÓVEL REAL

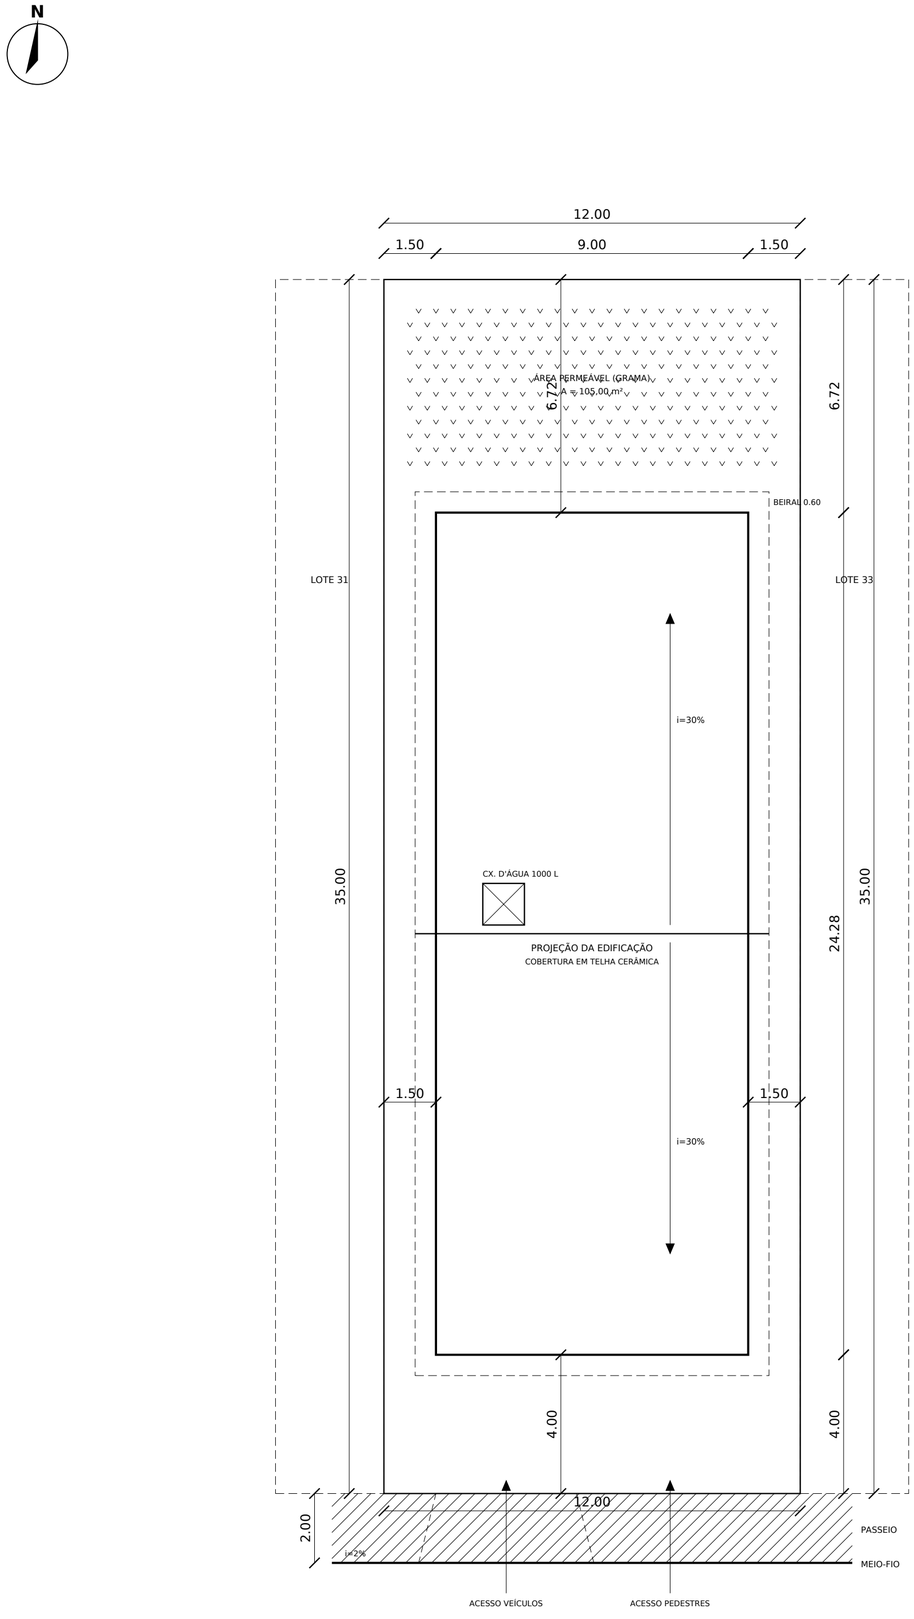


PLANTA DE SITUAÇÃO — ESCALA 1:125

QUADRO DE ÁREAS

DESCRIÇÃO	ÁREA / ÍNDICE
ÁREA DO TERRENO	420,00 m²
ÁREA CONSTRUÍDA TÉRREO	218,52 m²
ÁREA CONSTRUÍDA PAV. SUPERIOR	174,82 m²
ÁREA CONSTRUÍDA TOTAL	393,34 m²
ÁREA DE PROJEÇÃO	218,52 m²
ÁREA PERMEÁVEL	105,00 m²
TAXA DE OCUPAÇÃO	52,03 %
COEFICIENTE DE APROVEITAMENTO	0,94
TAXA DE PERMEABILIDADE	25,00 %

PLANTA DE LOCALIZAÇÃO

SEM ESCALA

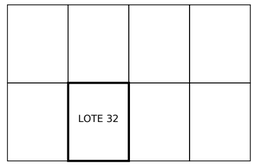

QUADRA E — Residencial da Conceição

ESCRITÓRIO

Oficina Monteiro Arquitetura

PROJETO

RESIDÊNCIA MARQUES

ENDEREÇO

Rua dos Jacarandás, 524

CONDOMÍNIO

Residencial da Conceição

LOTE / QUADRA

32 / E

MUNICÍPIO

Porto da Mota

MATRÍCULA

61.198 — 3º Ofício de Registro de Imóveis de Porto da Mota

PROPRIETÁRIO

Guilherme da Conceição Montenegro

AUTOR DO PROJETO

Manuella Novaes Araújo

REGISTRO

CAU A245952-8

RRT

10969117

CONTEÚDO

SITUAÇÃO E LOCALIZAÇÃO

PRANCHA

01/03

REVISÃO

R01

ESCALA

INDICADA

DATA

15/09/2026


AUTOR DO PROJETO

PROPRIETÁRIO

DOCUMENTO FICTÍCIO — BASE SINTÉTICA DO ARQUITETO AUDITOR — NÃO CORRESPONDE A IMÓVEL REAL


QUADRO DE ESQUADRIAS

P1	0,90 x 2,10	PORTA DE GIRO — ENTRADA
P2	0,80 x 2,10	PORTA DE GIRO — MADEIRA
P3	0,70 x 2,10	PORTA DE GIRO — ÁREAS MOLHADAS
PG	2,80 x 2,20	PORTÃO BASCULANTE
J1	1,50 x 1,20	JANELA DE CORRER — PEITORIL 1,00
J2	0,60 x 0,60	BASCULANTE — PEITORIL 1,60

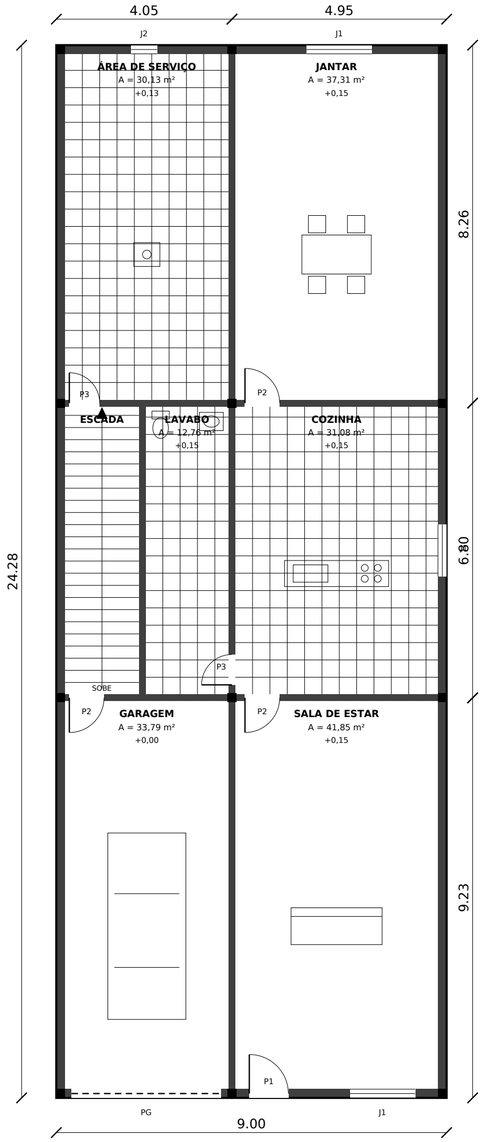

PLANTA BAIXA — TÉRREO — ESCALA 1:100

ÁREA: 218,52 m²

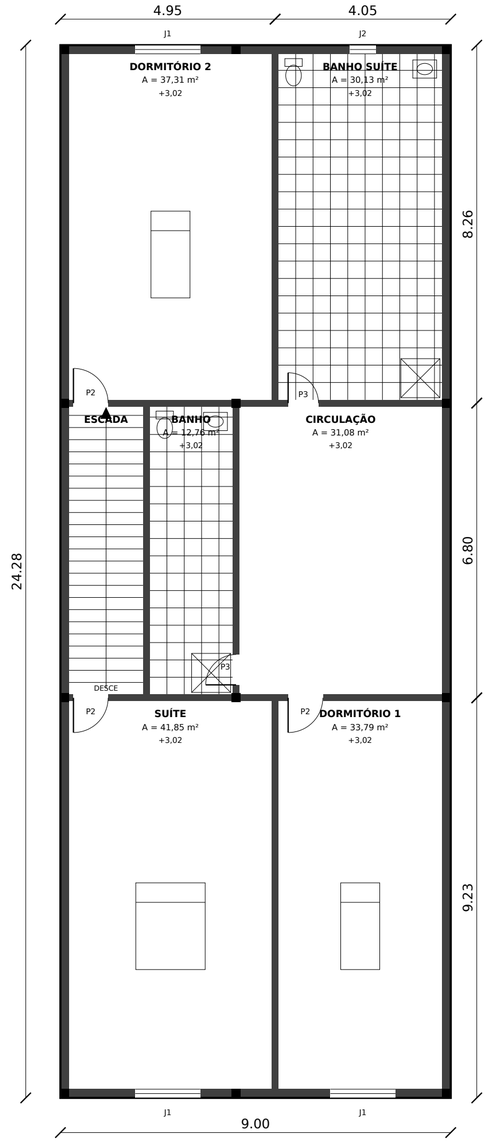

PLANTA BAIXA — PAVIMENTO SUPERIOR — ESCALA 1:100

ÁREA: 174,82 m²

ESCRITÓRIO

Oficina Monteiro Arquitetura

PROJETO

RESIDÊNCIA MARQUES

ENDEREÇO

Rua dos Jacarandás, 524

CONDOMÍNIO

Residencial da Conceição

LOTE / QUADRA

32 / E

MUNICÍPIO

Porto da Mota

MATRÍCULA

61.198 — 3º Ofício de Registro de Imóveis de Porto da Mota

PROPRIETÁRIO

Guilherme da Conceição Montenegro

AUTOR DO PROJETO

Manuella Novaes Araújo

REGISTRO

CAU A245952-8

RRT

10969117

CONTEÚDO

PLANTAS BAIXAS

PRANCHA

02/03

REVISÃO

R01

ESCALA

INDICADA


DATA

15/09/2026


AUTOR DO PROJETO

PROPRIETÁRIO

DOCUMENTO FICTÍCIO — BASE SINTÉTICA DO ARQUITETO AUDITOR — NÃO CORRESPONDE A IMÓVEL REAL

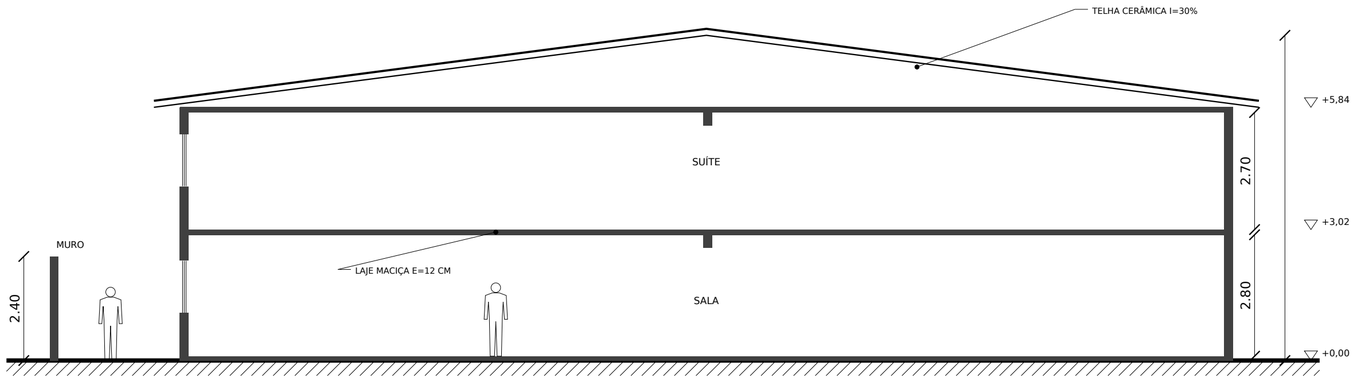

CORTE AA — ESCALA 1:100

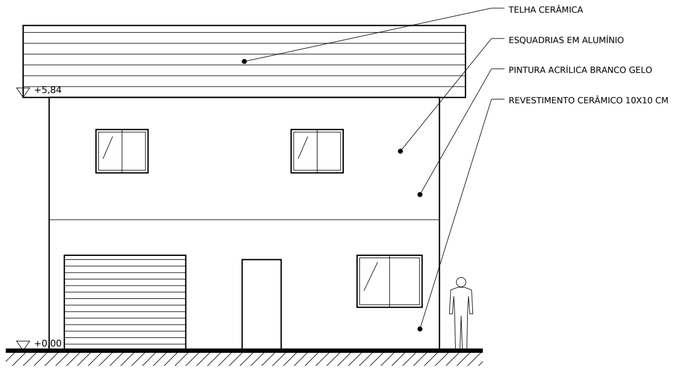

FACHADA FRONTAL — ESCALA 1:100

ESCRITÓRIO

Oficina Monteiro Arquitetura

PROJETO

RESIDÊNCIA MARQUES

ENDEREÇO

Rua dos Jacarandás, 524

CONDOMÍNIO

Residencial da Conceição

LOTE / QUADRA

32 / E

MUNICÍPIO

Porto da Mota

MATRÍCULA

61.198 — 3º Ofício de Registro de Imóveis de Porto da Mota

PROPRIETÁRIO

Guilherme da Conceição Montenegro

AUTOR DO PROJETO

Manuella Novaes Araújo

REGISTRO

CAU A245952-8

RRT

10969117

CONTEÚDO

CORTE E FACHADA

PRANCHA

03/03

REVISÃO

R01

ESCALA

INDICADA

DATA

15/09/2026

AUTOR DO PROJETO

PROPRIETÁRIO