DOCUMENTO FICTÍCIO — BASE SINTÉTICA DO ARQUITETO AUDITOR — NÃO CORRESPONDE A IMÓVEL REAL

RESIDENCIA MONTEIRO

PROJETO ARQUITETONICO - RESIDENCIA UNIFAMILIAR


PROPRIETARIO: LUCCA PIRES CORREIA. ENDERECO: ALAMEDA DOS JACARANDAS, 724, LOTE 27, QUADRA D, CONDOMINIO DIAS, NOVA CUNHA. MATRICULA N° 65.739 DO 1° OFICIO DE REGISTRO DE IMOVEIS DE NOVA CUNHA. AUTOR DO PROJETO: MATHIAS GONCALVES LEAO, CAU A111821-6. RRT N° 16995618.

FOLHAS

01 - CAPA
02 - SITUACAO E LOCALIZACAO
03 - PLANTAS BAIXAS
04 - CORTE E FACHADA
05 - PERSPECTIVA

DOCUMENTO FICTÍCIO — BASE SINTÉTICA DO ARQUITETO AUDITOR — NÃO CORRESPONDE A IMÓVEL REAL



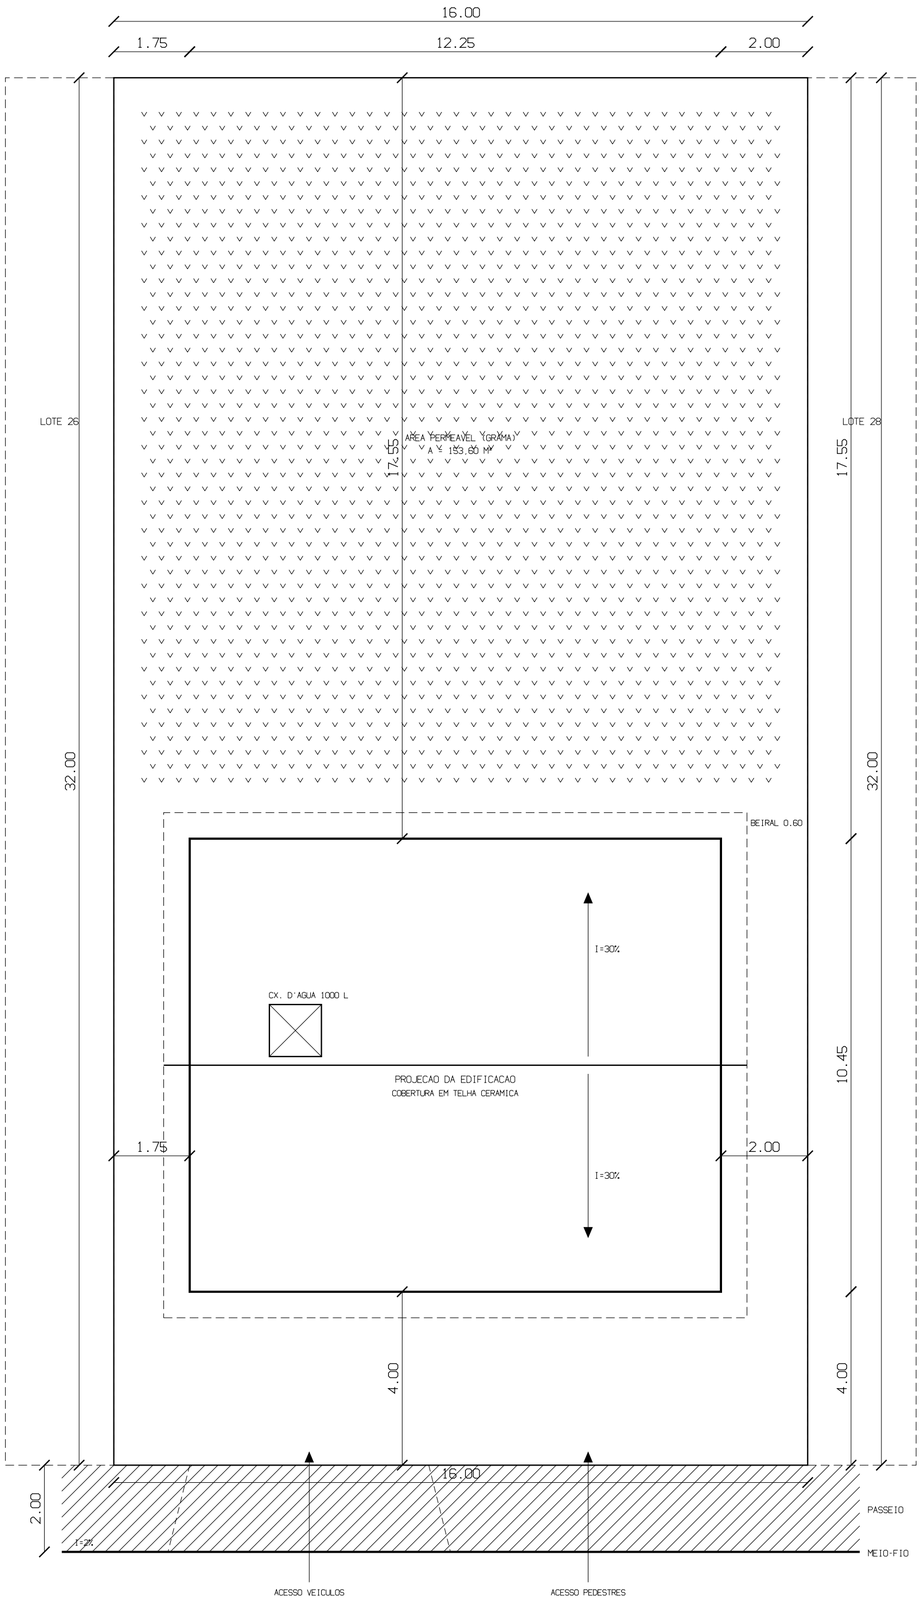

PLANTA DE SITUACAO - ESCALA 1:100

QUADRO DE AREAS

AREA DO TERRENO	A=509.70M²
AREA CONSTRUIDA TERREO	A=128.01M²
AREA CONSTRUIDA PAV. SUPERIOR	A=102.41M²
AREA CONSTRUIDA TOTAL	A=230.42M²
AREA DE PROJECAO	A=128.01M²
AREA PERMEAVEL	A=153.60M²
TAXA DE OCUPACAO	25.11%
COEFICIENTE DE APROVEITAMENTO	C=0.45
TAXA DE PERMEABILIDADE	30.14%
ALTURA DA EDIFICACAO	H=7.50M

PLANTA DE LOCALIZACAO

SEM ESCALA

LOTE 36 497.45 M²	LOTE 37 524.70 M²	LOTE 38 472.20 M²	LOTE 39 497.45 M²
LOTE 26 472.20 M²	LOTE 27 509.70 M²	LOTE 28 516.10 M²	LOTE 29 516.10 M²

QUADRA D - CONDOMINIO DIAS

02
05

ESCRITÓRIO:	ATELIE SAMPAIO ARQUITETURA
PROJETO:	RESIDENCIA MONTEIRO
ENDEREÇO:	ALAMEDA DOS JACARANDAS, 724
CONDOMÍNIO:	CONDOMINIO DIAS
LOTE / QUADRA:	27 / D
MUNICÍPIO:	NOVA CUNHA
MATRÍCULA:	65.739 - 1° OFICIO DE REGISTRO DE IMOVEIS DE NOVA CUNHA
PROPRIETÁRIO:	LUCCA PIRES CORREIA
AUTOR DO PROJETO:	MATHIAS GONCALVES LEAO
REGISTRO:	CAU A111821-6
RRT:	16995618
CONTEÚDO:	SITUACAO E LOCALIZACAO
PRANCHA:	
REVISÃO:	
ESCALA:	INDICADA
DATA:	15/09/2026


AUTOR DO PROJETO

PROPRIETÁRIO

DOCUMENTO FICTÍCIO — BASE SINTÉTICA DO ARQUITETO AUDITOR — NÃO CORRESPONDE A IMÓVEL REAL


QUADRO DE ESQUADRIAS

P1	0,90 X 2,10	PORTA DE GIRO - ENTRADA
P2	0,80 X 2,10	PORTA DE GIRO - MADEIRA
P3	0,70 X 2,10	PORTA DE GIRO - AREAS MOLHADAS
PG	2,80 X 2,20	PORTAO BASCULANTE
J1	1,50 X 1,20	JANELA DE CORRER - PEITORIL 1,00
J2	0,60 X 0,60	BASCULANTE - PEITORIL 1,60

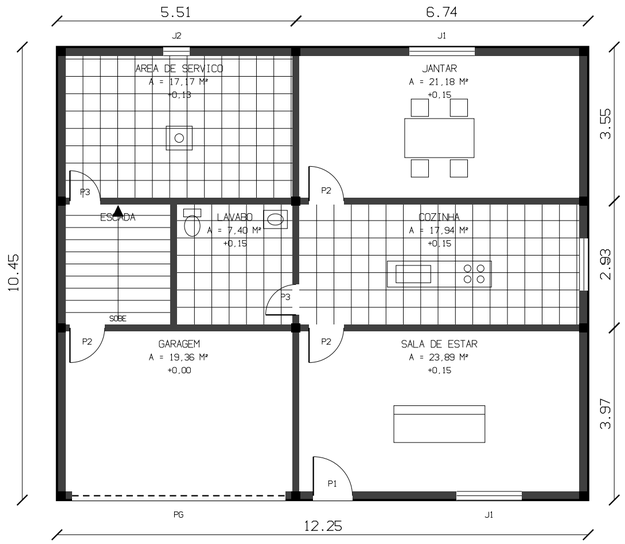

PLANTA BAIXA - TERREO - ESCALA 1:100

AREA: 128,01 M²

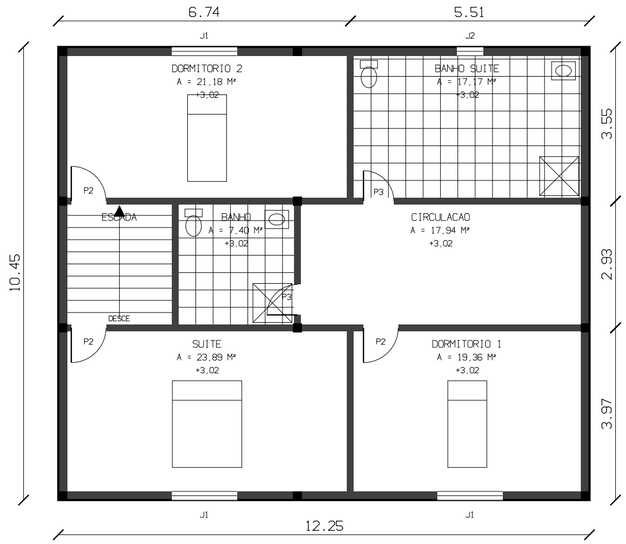

PLANTA BAIXA - PAVIMENTO SUPERIOR - ESCALA 1:100

AREA: 102,41 M²


03
05

ESCRITÓRIO:	ATELIE SAMPAIO ARQUITETURA
PROJETO:	RESIDENCIA MONTEIRO
ENDEREÇO:	ALAMEDA DOS JACARANDAS, 724
CONDOMÍNIO:	CONDOMINIO DIAS
LOTE / QUADRA:	27 / D
MUNICÍPIO:	NOVA CUNHA
MATRÍCULA:	65.739 - 1° OFICIO DE REGISTRO DE IMOVEIS DE NOVA CUNHA
PROPRIETÁRIO:	LUCCA PIRES CORREIA
AUTOR DO PROJETO:	MATHIAS GONCALVES LEAO
REGISTRO:	CAU A111821-6
RRT:	16995618
CONTEÚDO:	PLANTAS BAIXAS
PRANCHA:	
REVISÃO:	
ESCALA:	INDICADA
DATA:	15/09/2026


AUTOR DO PROJETO

PROPRIETÁRIO

DOCUMENTO FICTÍCIO — BASE SINTÉTICA DO ARQUITETO AUDITOR — NÃO CORRESPONDE A IMÓVEL REAL

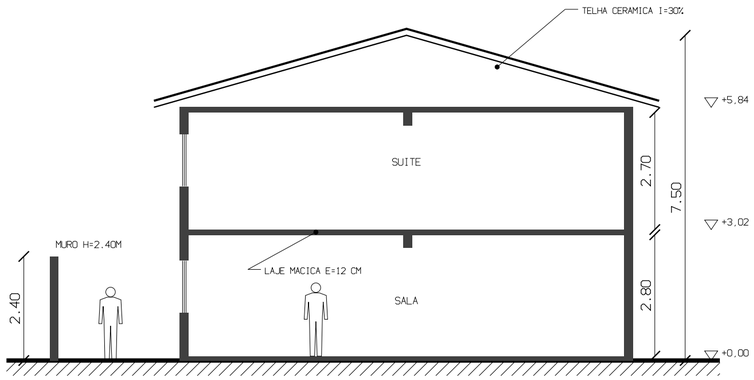

CORTE AA - ESCALA 1:100

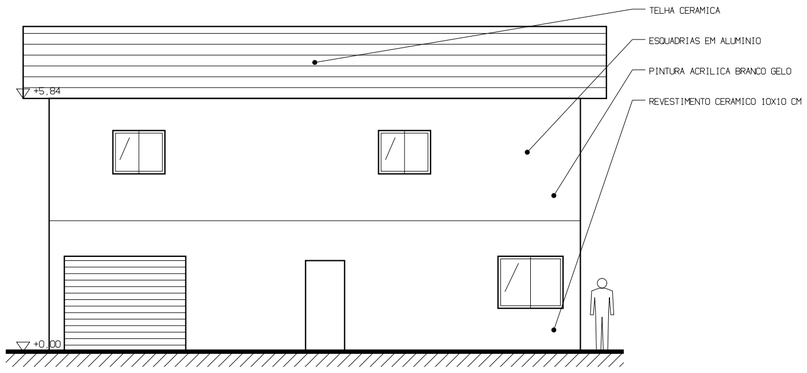

FACHADA FRONTAL - ESCALA 1:100


04

05

ESCRITÓRIO:	ATELIE SAMPAIO ARQUITETURA
PROJETO:	RESIDENCIA MONTEIRO
ENDEREÇO:	ALAMEDA DOS JACARANDAS, 724
CONDOMÍNIO:	CONDOMINIO DIAS
LOTE / QUADRA:	27 / D
MUNICÍPIO:	NOVA CUNHA
MATRÍCULA:	65.739 - 1° OFICIO DE REGISTRO DE IMOVEIS DE NOVA CUNHA
PROPRIETÁRIO:	LUCCA PIRES CORREIA
AUTOR DO PROJETO:	MATHIAS GONCALVES LEAO
REGISTRO:	CAU A111821-6
RRT:	16995618
CONTEÚDO:	CORTE E FACHADA
PRANCHA:	
REVISÃO:	
ESCALA:	INDICADA
DATA:	15/09/2026

AUTOR DO PROJETO

PROPRIETÁRIO

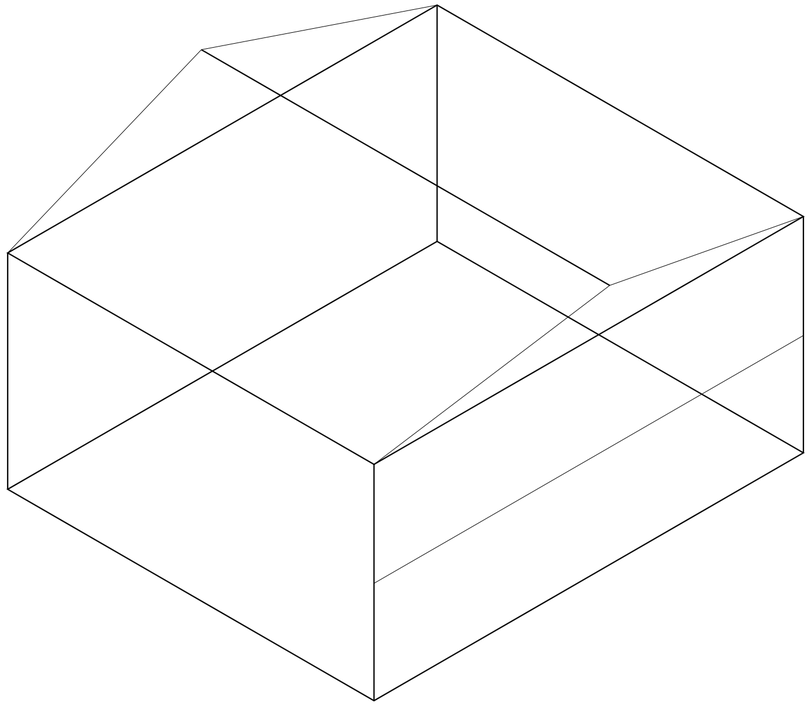

FICTICIO