
DOCUMENTO FICTÍCIO — BASE SINTÉTICA DO ARQUITETO AUDITOR — NÃO CORRESPONDE A IMÓVEL REAL



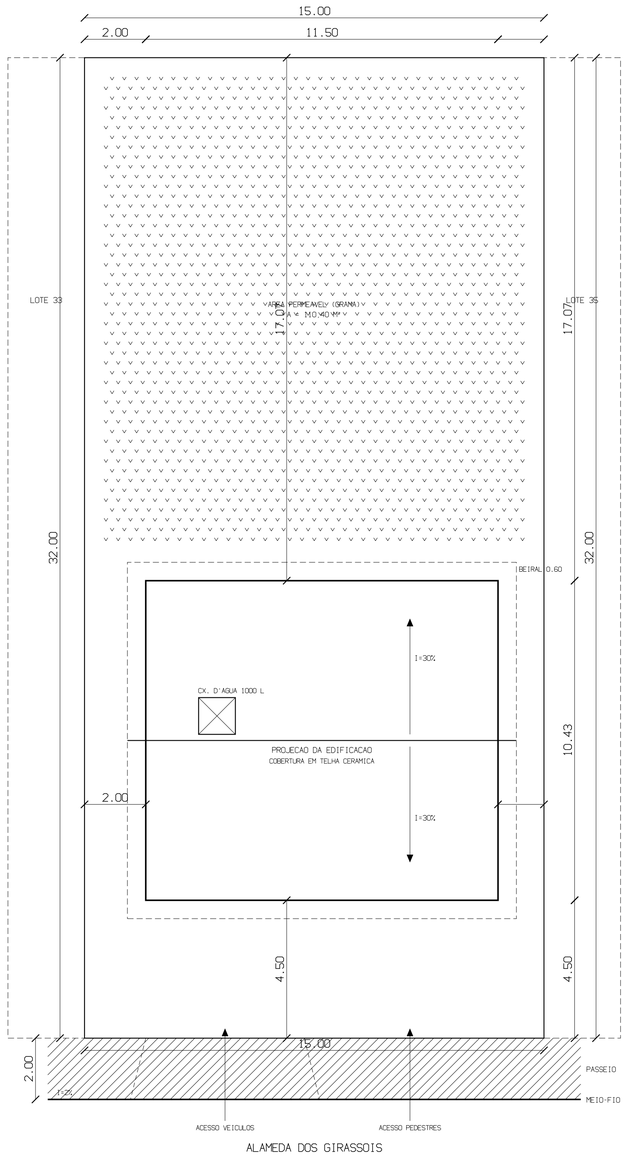

ALAMEDA DOS GIRASSOIS

QUADRO DE ÁREAS

ÁREA DO TERRENO	A=480.00M²
ÁREA CONSTRUÍDA TÉRREO	A=119.94M²
ÁREA CONSTRUÍDA PAV. SUPERIOR	A=95.95M²
ÁREA CONSTRUÍDA TOTAL	A=215.89M²
ÁREA DE PROJEÇÃO	A=119.94M²
ÁREA PERMEÁVEL	A=110.40M²
TAXA DE OCUPAÇÃO	24.99%
COEFICIENTE DE APROVEITAMENTO	C=0.45
TAXA DE PERMEABILIDADE	23.00%
ALTURA DA EDIFICAÇÃO	H=6.50M

PLANTA DE LOCALIZAÇÃO

SEM ESCALA

LOTE 43 475.20 M²	LOTE 44 467.75 M²	LOTE 45 467.75 M²	LOTE 46 442.50 M²
LOTE 33 467.75 M²	LOTE 34 480.00 M²	LOTE 35 475.20 M²	LOTE 36 467.75 M²

QUADRA H - JARDINS DO RIOS

PLANTA DE SITUAÇÃO - ESCALA 1:100

ESCRITÓRIO GRUPO CASTRO ARQUITETURA	PROJETO RESIDÊNCIA PACHECO	ENDEREÇO ALAMEDA DOS GIRASSOIS, 236	CONDOMÍNIO JARDINS DO RIOS	LOTE / QUADRA 34 / H
MUNICÍPIO CAMPO MENDES	MATRÍCULA 76.995 - 1° OFÍCIO DE REGISTRO DE IMÓVEIS DE CAMPO MENDES	PROPRIETÁRIO LAURA SÁ RIBEIRO	AUTOR DO PROJETO ANA CLARA SAMPAIO MARTINS	REGISTRO CAU A166687-7
ART 17062335	CONTEÚDO SITUAÇÃO E LOCALIZAÇÃO	PRANCHA 01/04	REVISÃO R00	ESCALA INDICADA
DATA 15/09/2026				