
DOCUMENTO FICTÍCIO — BASE SINTÉTICA DO ARQUITETO AUDITOR — NÃO CORRESPONDE A IMÓVEL REAL

N

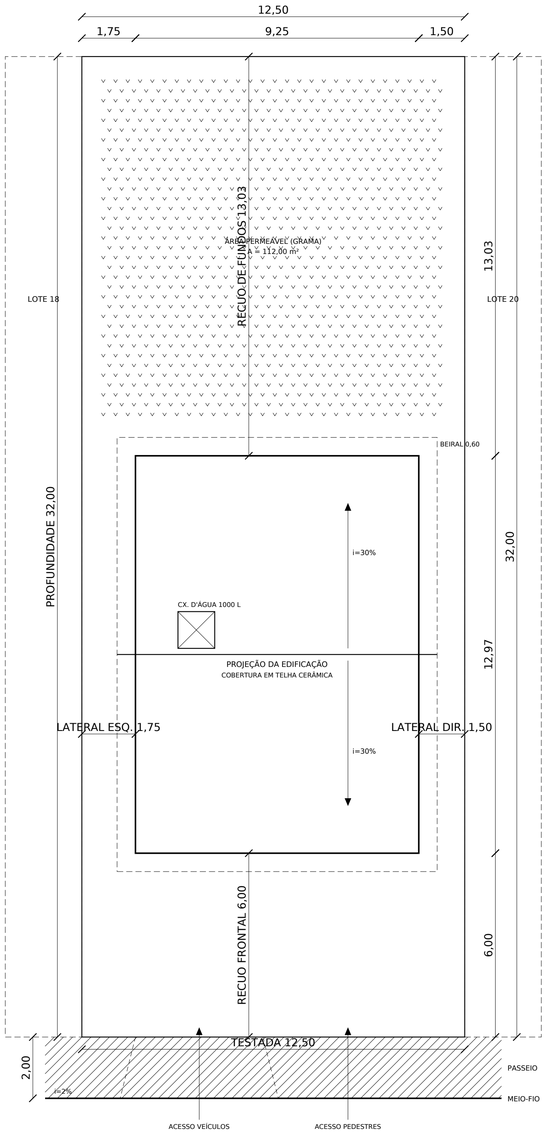


PLANTA DE SITUAÇÃO — ESCALA 1:100

QUADRO DE ÁREAS

DESCRIÇÃO	ÁREA / ÍNDICE
ÁREA DO TERRENO	400,00 m²
ÁREA CONSTRUÍDA TÉRREO	119,97 m²
ÁREA CONSTRUÍDA PAV. SUPERIOR	95,98 m²
ÁREA CONSTRUÍDA TOTAL	215,95 m²
ÁREA DE PROJEÇÃO	119,97 m²
ÁREA PERMEÁVEL	112,00 m²
TAXA DE OCUPAÇÃO	29,99 %
COEFICIENTE DE APROVEITAMENTO	0,54
TAXA DE PERMEABILIDADE	28,00 %

PLANTA DE LOCALIZAÇÃO

SEM ESCALA

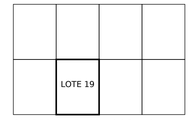

QUADRA H — Residencial Correia

ESCRITÓRIO:	Oficina Câmara Arquitetura
PROJETO:	RESIDÊNCIA NOGUEIRA
ENDEREÇO:	Alameda dos Jacarandás, 949
CONDOMÍNIO:	Residencial Correia
LOTE / QUADRA:	19 / H
MUNICÍPIO:	Serra Pacheco
MATRÍCULA:	71.677 — 3º Ofício de Registro de Imóveis de Serra Pacheco
PROPRIETÁRIO:	Milena Cunha Pereira
AUTOR DO PROJETO:	Elisa Martins Aragão
REGISTRO:	CAU A198048-7
RRT:	10814047
CONTEÚDO:	SITUAÇÃO E LOCALIZAÇÃO
PRANCHA:	01/03
REVISÃO:	R00
ESCALA:	INDICADA
DATA:	15/09/2026


AUTOR DO PROJETO

PROPRIETÁRIO


DOCUMENTO FICTÍCIO — BASE SINTÉTICA DO ARQUITETO AUDITOR — NÃO CORRESPONDE A IMÓVEL REAL

QUADRO DE ESQUADRIAS

P1	0,90 x 2,10	PORTA DE GIRO — ENTRADA
P2	0,80 x 2,10	PORTA DE GIRO — MADEIRA
P3	0,70 x 2,10	PORTA DE GIRO — ÁREAS MOLHADAS
PG	2,80 x 2,20	PORTÃO BASCULANTE
J1	1,50 x 1,20	JANELA DE CORRER — PEITORIL 1,00
J2	0,60 x 0,60	BASCULANTE — PEITORIL 1,60

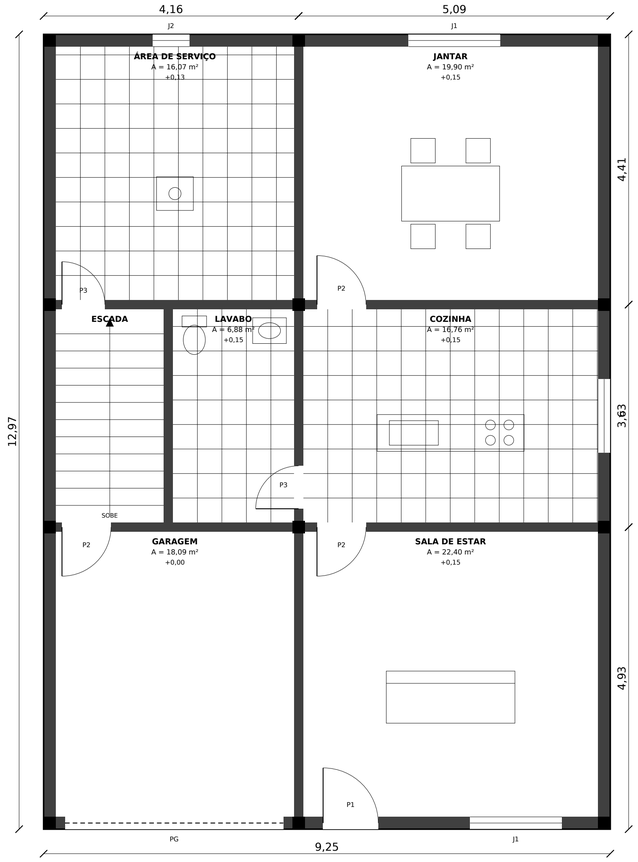

PLANTA BAIXA — TÉRREO — ESCALA 1:50
ÁREA: 119,97 m²

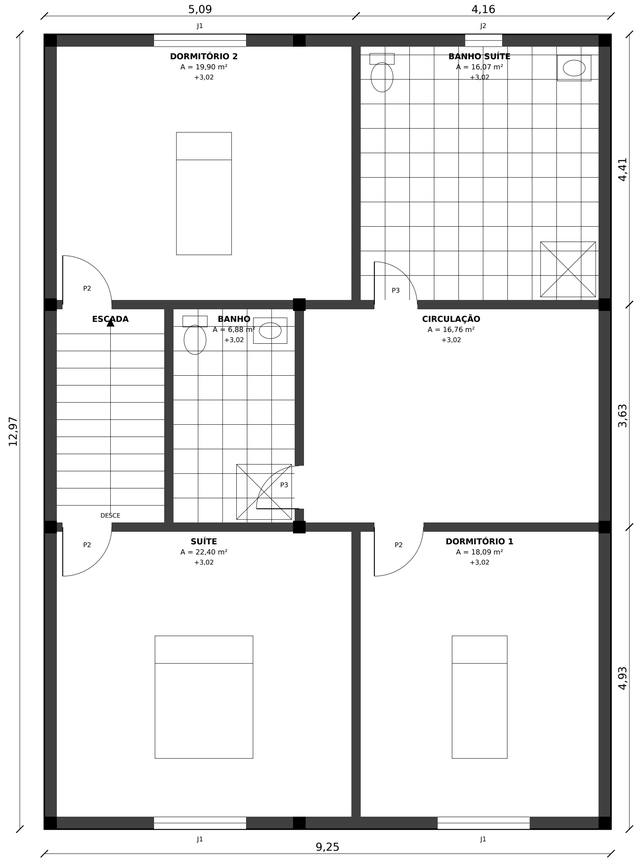


PLANTA BAIXA — PAVIMENTO SUPERIOR — ESCALA 1:50
ÁREA: 95,98 m²

ESCRITÓRIO:	Oficina Câmara Arquitetura
PROJETO:	RESIDÊNCIA NOGUEIRA
ENDEREÇO:	Alameda dos Jacarandás, 949
CONDOMÍNIO:	Residencial Correia
LOTE / QUADRA:	19 / H
MUNICÍPIO:	Serra Pacheco
MATRÍCULA:	71.677 — 3º Ofício de Registro de Imóveis de Serra Pacheco
PROPRIETÁRIO:	Milena Cunha Pereira
AUTOR DO PROJETO:	Elisa Martins Aragão
REGISTRO:	CAU A198048-7
RRT:	10814047
CONTEÚDO:	PLANTAS BAIXAS
PRANCHA:	02/03
REVISÃO:	R00
ESCALA:	INDICADA
DATA:	15/09/2026


AUTOR DO PROJETO

PROPRIETÁRIO

DOCUMENTO FICTÍCIO — BASE SINTÉTICA DO ARQUITETO AUDITOR — NÃO CORRESPONDE A IMÓVEL REAL

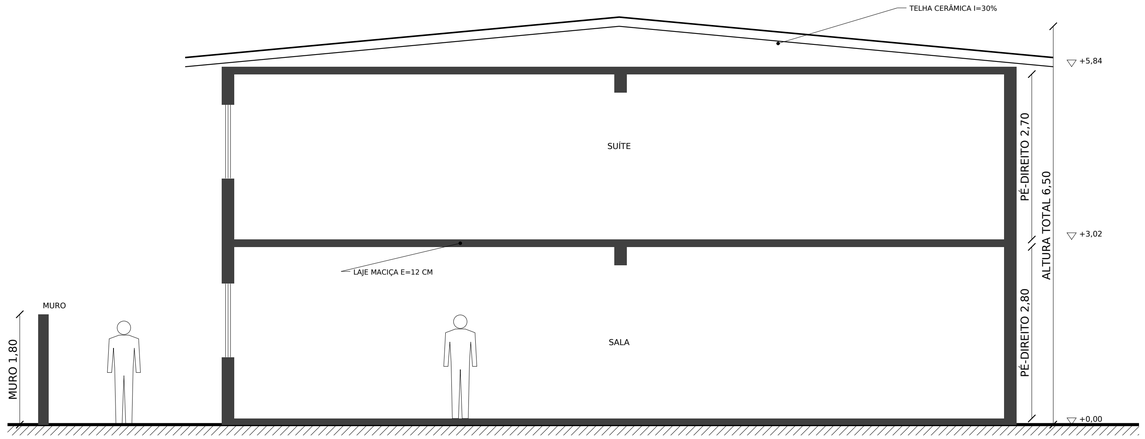

CORTE AA — ESCALA 1:50

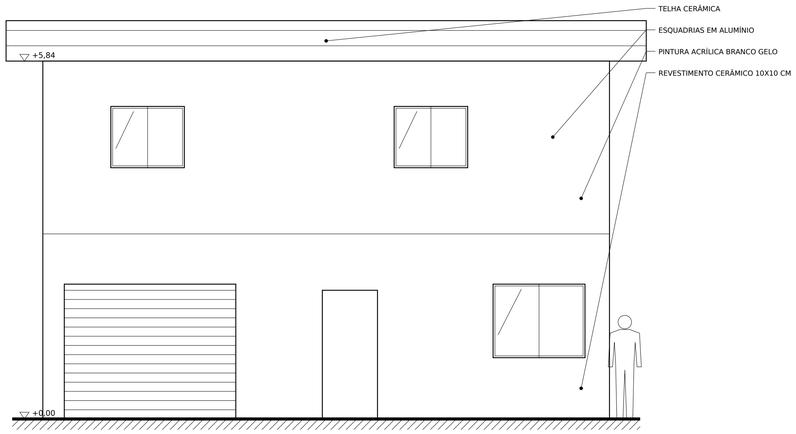

FACHADA FRONTAL — ESCALA 1:50

ESCRITÓRIO:	Oficina Câmara Arquitetura
PROJETO:	RESIDÊNCIA NOGUEIRA
ENDEREÇO:	Alameda dos Jacarandás, 949
CONDOMÍNIO:	Residencial Correia
LOTE / QUADRA:	19 / H
MUNICÍPIO:	Serra Pacheco
MATRÍCULA:	71.677 — 3º Ofício de Registro de Imóveis de Serra Pacheco
PROPRIETÁRIO:	Milena Cunha Pereira
AUTOR DO PROJETO:	Elisa Martins Aragão
REGISTRO:	CAU A198048-7
RRT:	10814047
CONTEÚDO:	CORTE E FACHADA
PRANCHA:	03/03
REVISÃO:	R00
ESCALA:	INDICADA
DATA:	15/09/2026

AUTOR DO PROJETO

PROPRIETÁRIO