

DOCUMENTO FICTÍCIO — BASE SINTÉTICA DO ARQUITETO AUDITOR — NÃO CORRESPONDE A IMÓVEL REAL

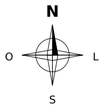

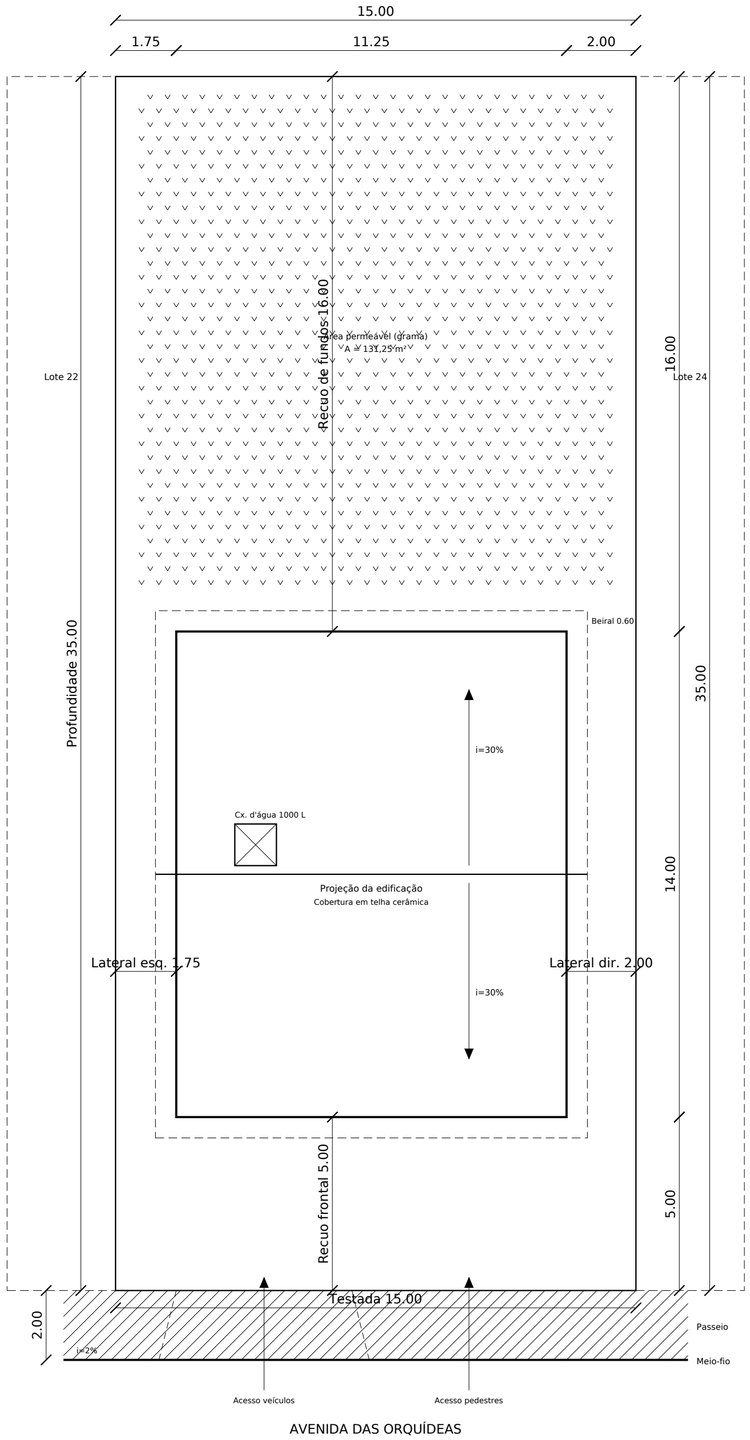

Planta de situação — Escala 1:125

Quadro de áreas


Áreas (m²)

Área do terreno	Área construída térreo	Área construída pav. superior
525,00	**157,50**	**126,00**
Área construída total	**Área de projeção**	**Área permeável**
293,50	**157,50**	**131,25**

T.O. = 30,00% C.A. = 0,56 T.P. = 25,00%

Planta de localização

Sem escala

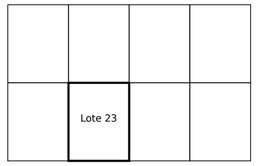

Quadra C — Condomínio Ferreira

Escritório:	Ateliê Farias Arquitetura
Projeto:	RESIDÊNCIA PACHECO
Endereço:	Avenida das Orquídeas, 177
Condomínio:	Condomínio Ferreira
Lote / Quadra:	23 / C
Município:	Serra Pastor
Matrícula:	77.116 — 1º Ofício de Registro de Imóveis de Serra Pastor
Proprietário:	Sabrina Vargas Oliveira
Autor do projeto:	Henrique Abreu das Neves
Registro:	CAU A66847-0
RRT:	15238161
Conteúdo:	Situação e localização
Prancha:	01/03
Revisão:	R00
Escala:	Indicada
Data:	15/09/2026


Autor do projeto

Proprietário

DOCUMENTO FICTÍCIO — BASE SINTÉTICA DO ARQUITETO AUDITOR — NÃO CORRESPONDE A IMÓVEL REAL


Quadro de esquadrias

P1	0,90 x 2,10	Porta de giro — entrada
P2	0,80 x 2,10	Porta de giro — madeira
P3	0,70 x 2,10	Porta de giro — áreas molhadas
PG	2,80 x 2,20	Portão basculante
J1	1,50 x 1,20	Janela de correr — peitoril 1,00
J2	0,60 x 0,60	Basculante — peitoril 1,60

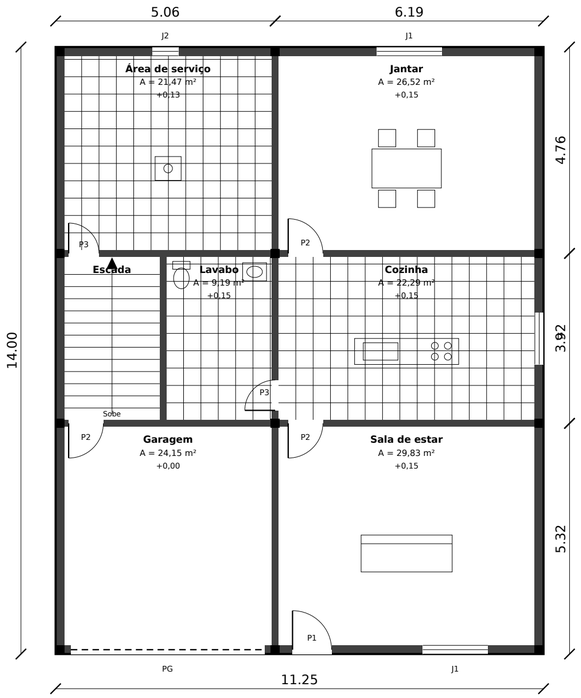

Planta baixa — térreo — Escala 1:100

Área: 157,50 m²

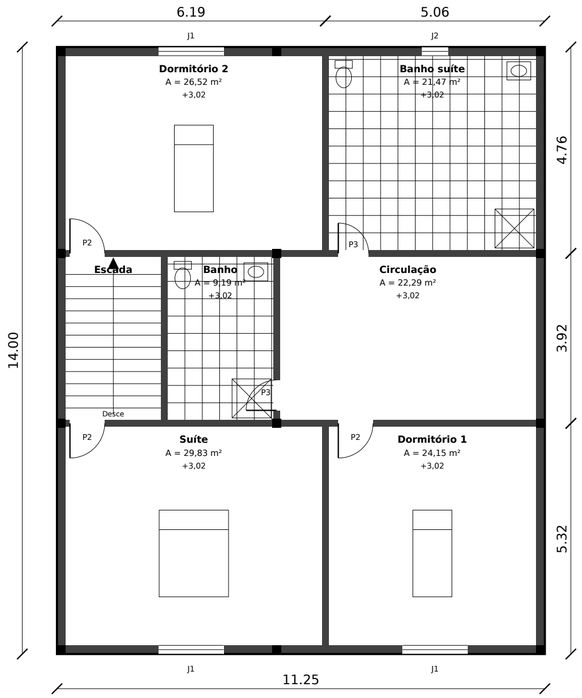

Planta baixa — pavimento superior — Escala 1:100


Área: 126,00 m²

Escritório:	Ateliê Farias Arquitetura
Projeto:	RESIDÊNCIA PACHECO
Endereço:	Avenida das Orquídeas, 177
Condomínio:	Condomínio Ferreira
Lote / Quadra:	23 / C
Município:	Serra Pastor
Matrícula:	77.116 — 1º Ofício de Registro de Imóveis de Serra Pastor
Proprietário:	Sabrina Vargas Oliveira
Autor do projeto:	Henrique Abreu das Neves
Registro:	CAU A66847-0
RRT:	15238161
Conteúdo:	Plantas baixas
Prancha:	02/03
Revisão:	R01
Escala:	Indicada
Data:	15/09/2026


Autor do projeto

Proprietário

DOCUMENTO FICTÍCIO — BASE SINTÉTICA DO ARQUITETO AUDITOR — NÃO CORRESPONDE A IMÓVEL REAL

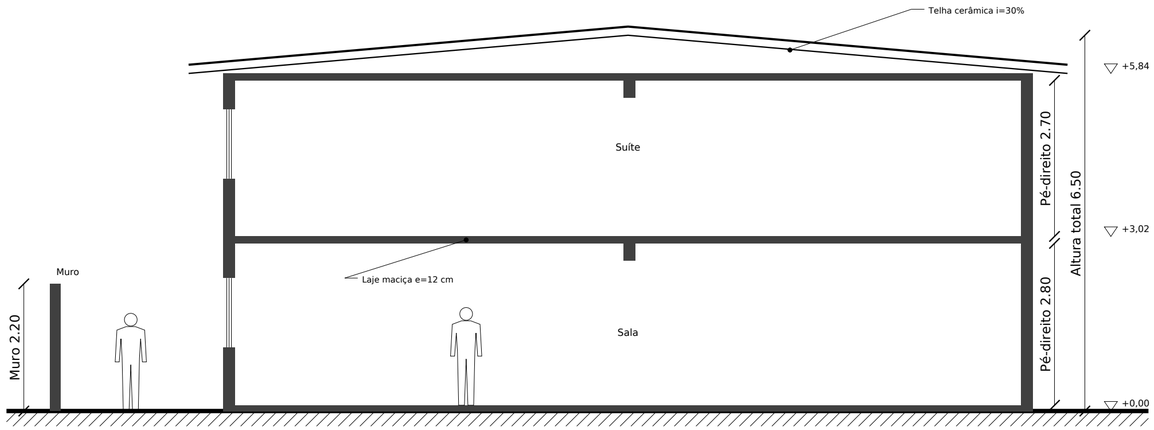

Corte AA — Escala 1:75

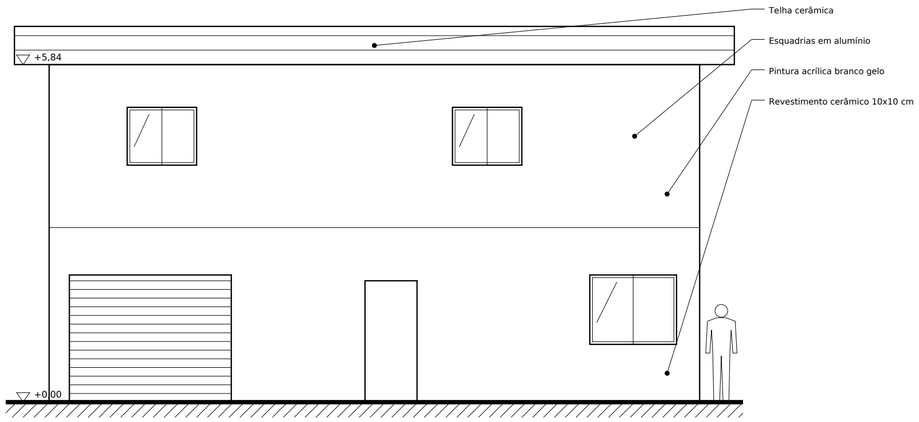

Fachada frontal — Escala 1:75

Escritório:	Ateliê Farias Arquitetura
Projeto:	RESIDÊNCIA PACHECO
Endereço:	Avenida das Orquídeas, 177
Condomínio:	Condomínio Ferreira
Lote / Quadra:	23 / C
Município:	Serra Pastor
Matrícula:	77.116 — 1º Ofício de Registro de Imóveis de Serra Pastor
Proprietário:	Sabrina Vargas Oliveira
Autor do projeto:	Henrique Abreu das Neves
Registro:	CAU A66847-0
RRT:	15238161
Conteúdo:	Corte e fachada
Prancha:	03/03
Revisão:	R00
Escala:	Indicada
Data:	15/09/2026

Autor do projeto

Proprietário