
DOCUMENTO FICTÍCIO — BASE SINTÉTICA DO ARQUITETO AUDITOR — NÃO CORRESPONDE A IMÓVEL REAL

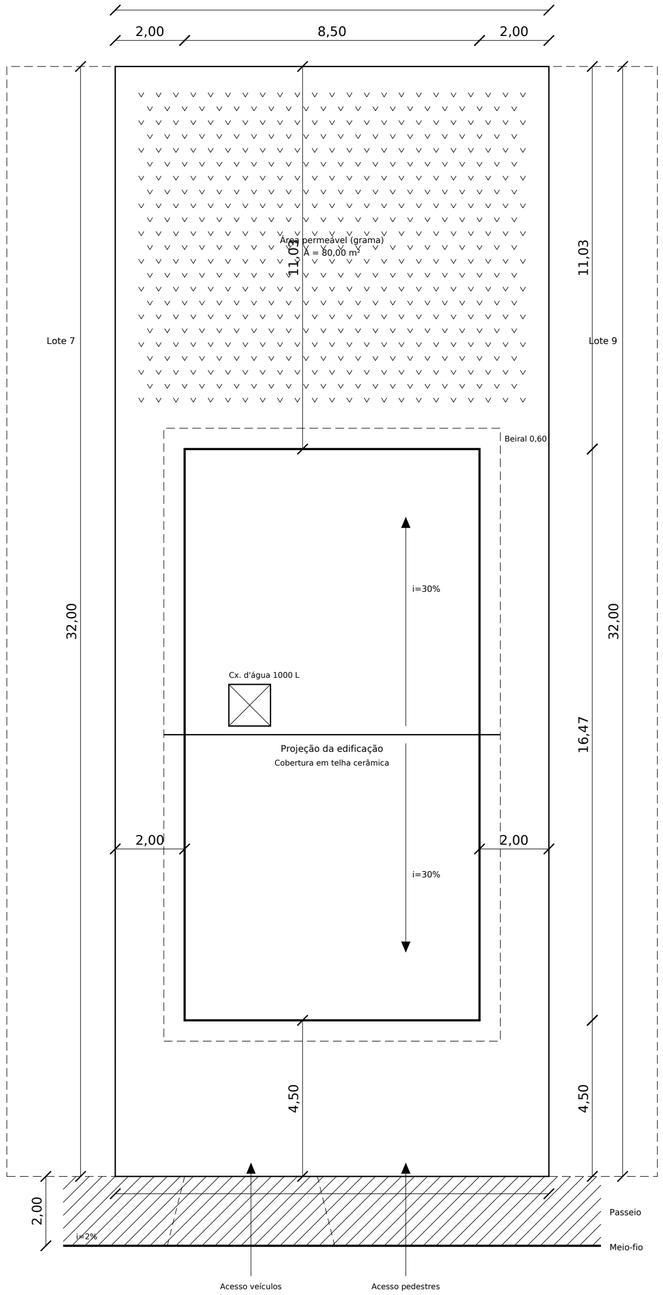

ALAMEDA DAS HORTÊNSIAS

Planta de situação — Escala 1:125

Quadro de áreas

Descrição	Área / índice
Área do terreno	397,70 m²
Área construída térreo	140,00 m²
Área construída pav. superior	112,00 m²
Área construída total	252,00 m²
Área de projeção	140,00 m²
Área permeável	80,00 m²
Taxa de ocupação	35,20 %
Coeficiente de aproveitamento	0,63
Taxa de permeabilidade	20,12 %

Planta de localização

Sem escala

Quadra E — Jardins do Pinto

Escritório **Ateliê Nogueira Arquitetura**	Projeto **RESIDÊNCIA PACHECO**	Endereço **Alameda das Hortênsias, 567**	Condomínio **Jardins do Pinto**	Lote / Quadra **8 / E**
Município **Nova da Cruz**	Matrícula **77.190 — 2º Ofício de Registro de Imóveis de Nova da Cruz**	Proprietário **Ana Luiza Carvalho Lima**	Autor do projeto **Laís Mendes Teixeira**	Registro **CAU A232968-7**
RRT **15183888**	Conteúdo **Situação e localização**	Prancha **01/03**	Revisão **R00**	Escala **Indicada**
Data **15/09/2026**				